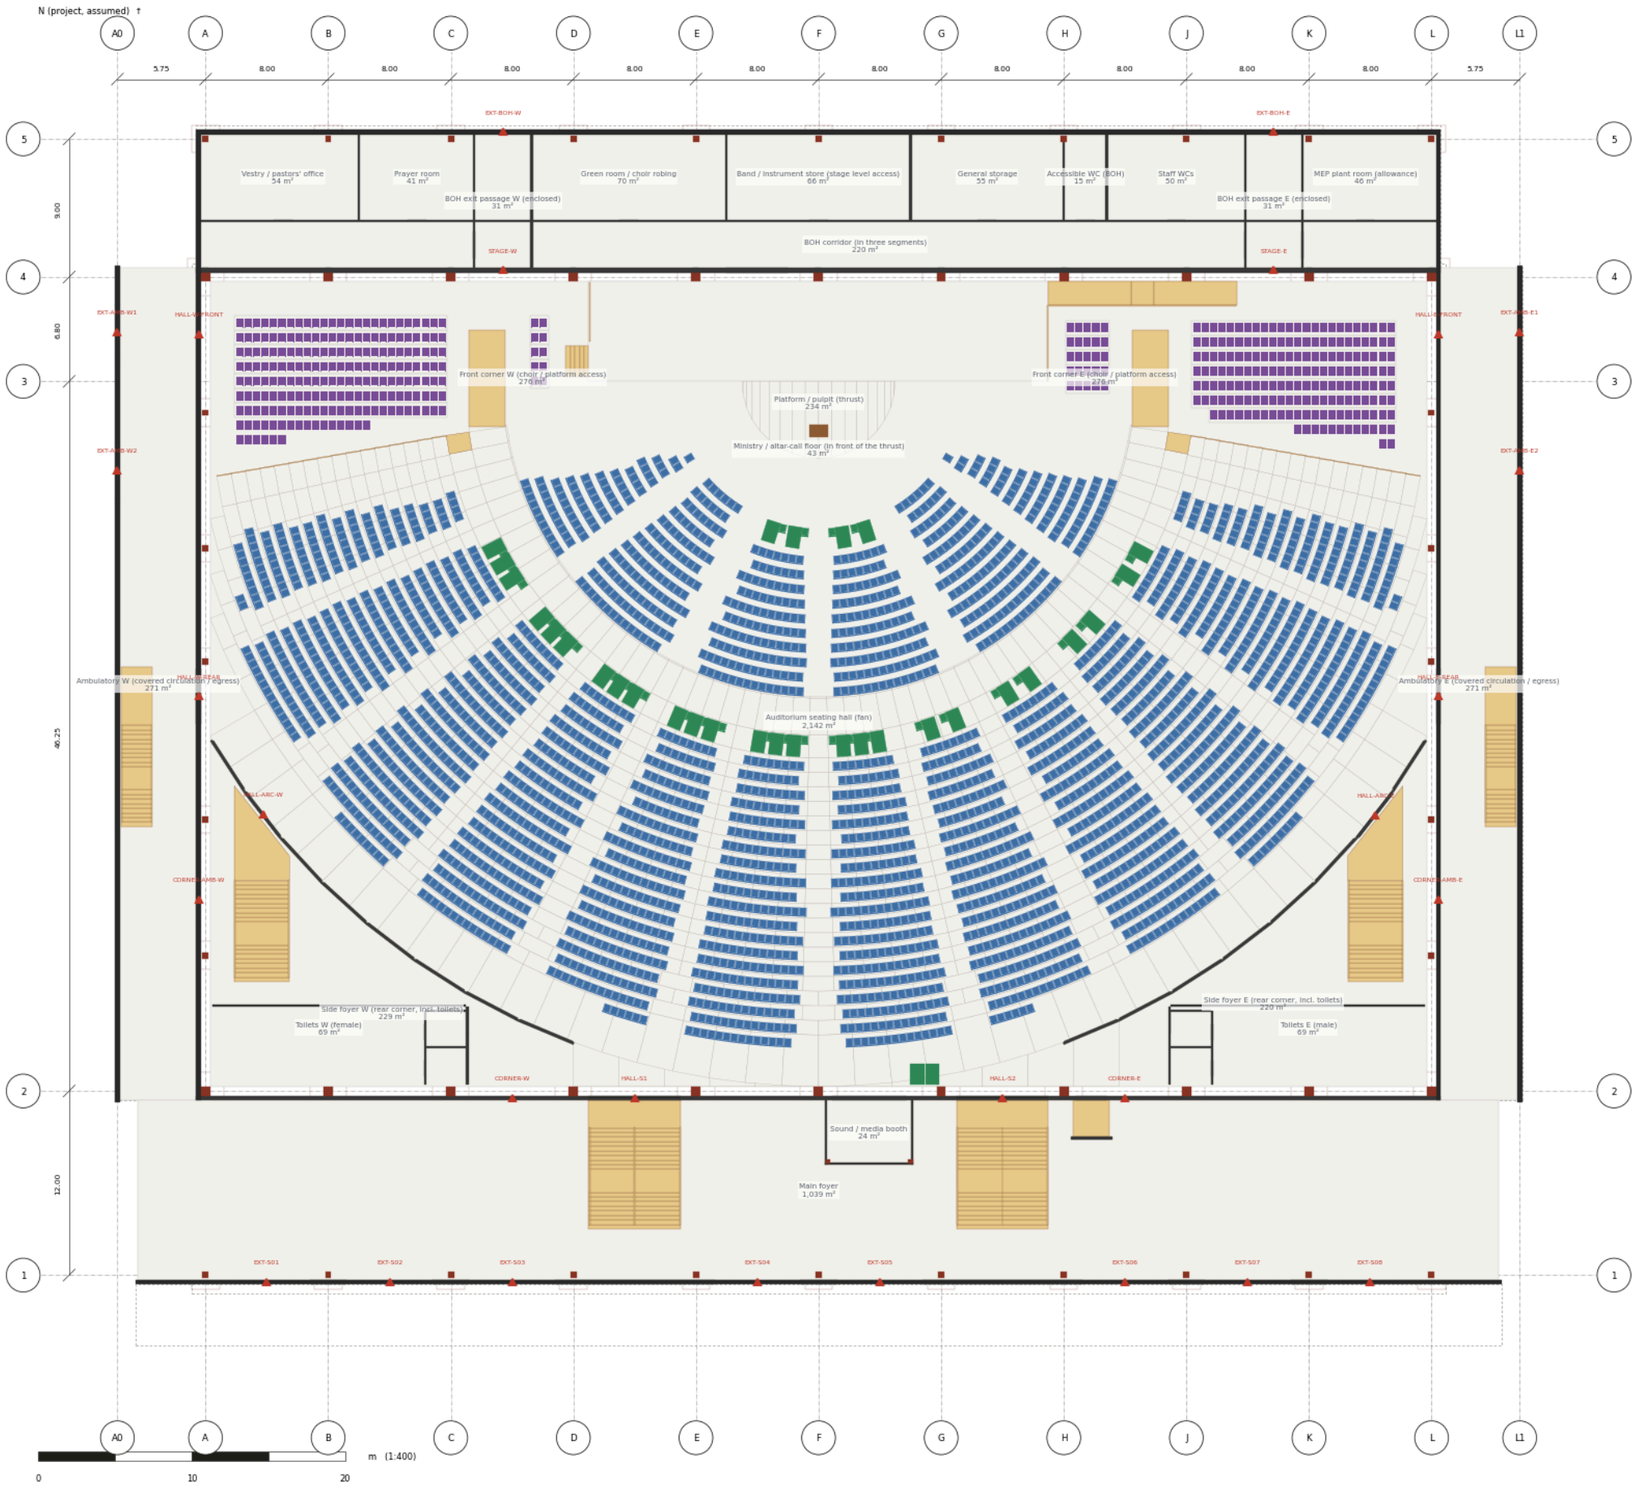


PROJECT

3,000-Seat Church Auditorium - Option B (long-side stage) Coordination Concept

DESIGN

B-long-side-stage

MODEL REVISION

B03-44bc3ae457

DRAWING

Ground floor plan

Plan at L00, cut below the roof structure

SCALE

1:400 at A3

SHEET

B-P100

SOURCE

`blender_manifest.json sha256 356464e19ccc094f`


UNITS

metres; levels in m above L00

STATUS

CONCEPT - UNVERIFIED - NOT FOR CONSTRUCTION

Concept coordination drawing generated from the Blender model. Not for construction. Dimensions unverified pending professional review.

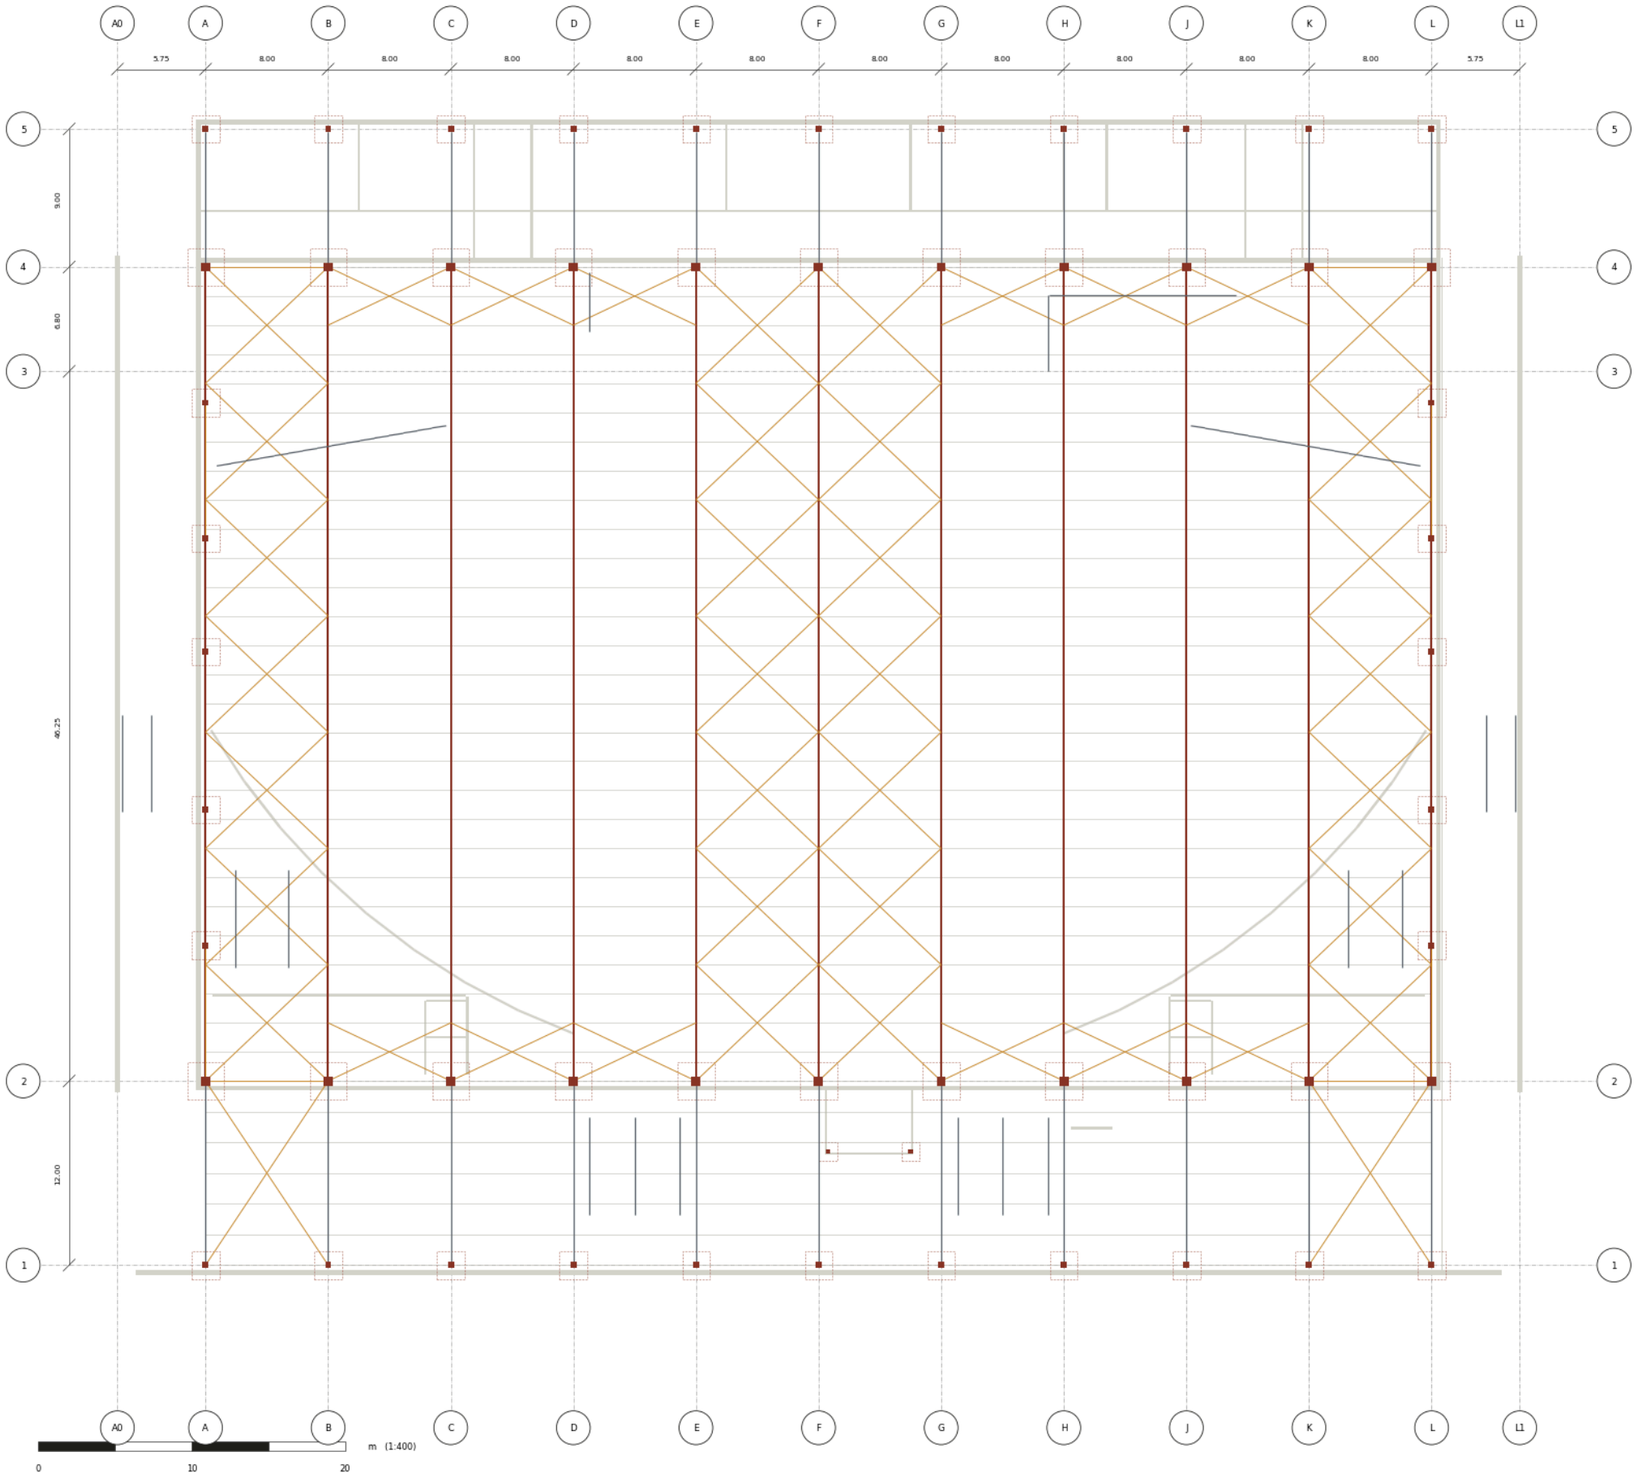

PROJECT

3,000-Seat Church Auditorium - Option B (long-side stage) Coordination Concept

DESIGN

B-long-side-stage

MODEL REVISION

B03-44bc3ae457

DRAWING

Structural grid and roof framing

Columns, pad footings (dashed), trusses, purlins and bracing

SCALE

1:400 at A3

SHEET

B-S100

SOURCE

`blender_manifest.json sha256 356464e19ccc094f`

UNITS

metres; levels in m above L00


STATUS


CONCEPT - UNVERIFIED - NOT FOR CONSTRUCTION

Concept coordination drawing generated from the Blender model. Not for construction. Dimensions unverified pending professional review.


08 · DRAWINGS

Building sections

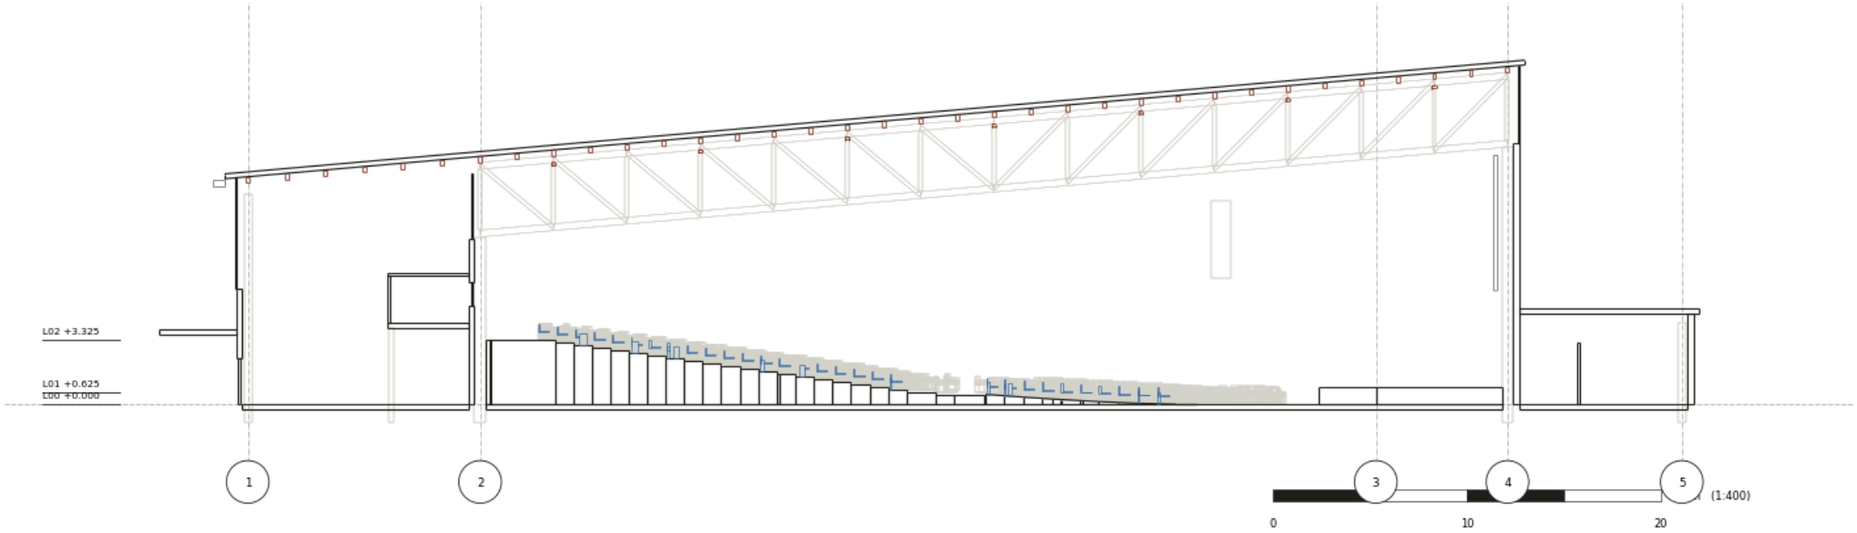

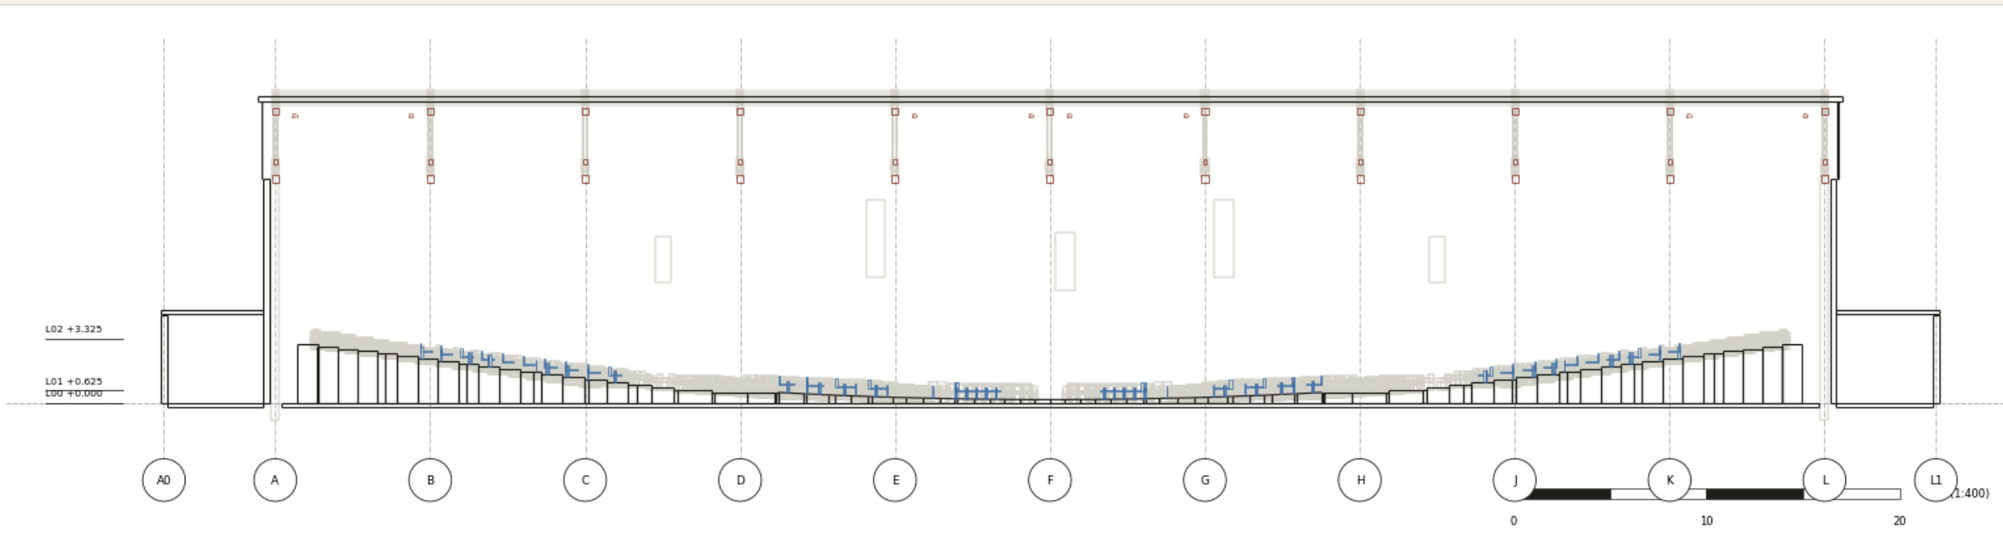

Sections A-A and B-B from the saved Option B model · schematic, concept status

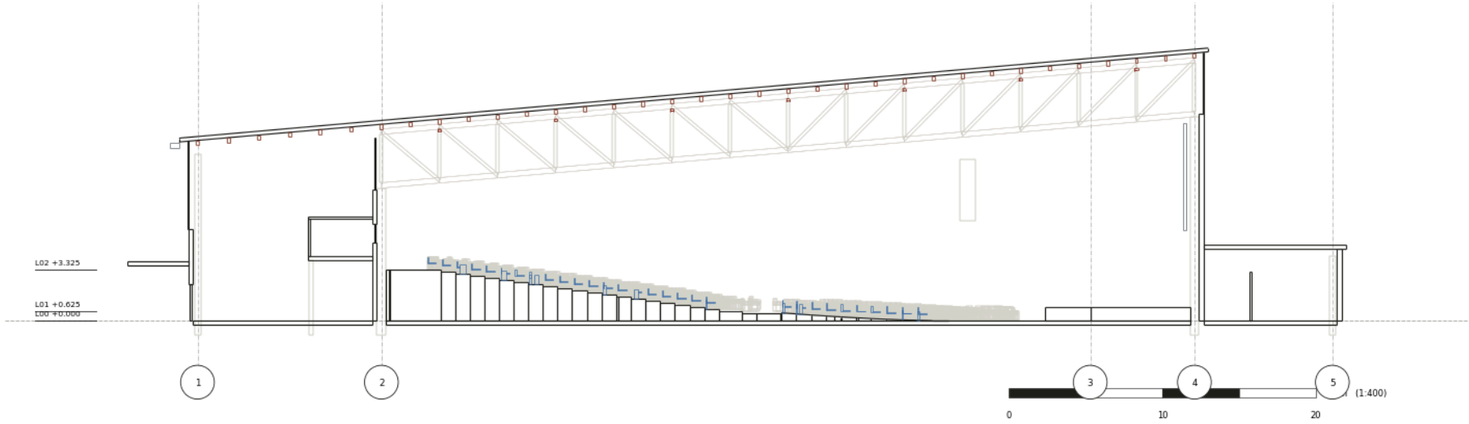

PROJECT

3,000-Seat Church Auditorium - Option B (long-side stage) Coordination Concept

DESIGN

B-long-side-stage

MODEL REVISION

B03-44bc3ae457

DRAWING

Section A-A

Cut on x = 44.00 m, looking towards +x

SCALE

1:400 at A3

SHEET

B-S300

SOURCE

blender_manifest.json sha256 356464e19ccc094f

UNITS

metres; levels in m above L00

STATUS

CONCEPT - UNVERIFIED - NOT FOR CONSTRUCTION

Concept coordination drawing generated from the Blender model. Not for construction. Dimensions unverified pending professional review.